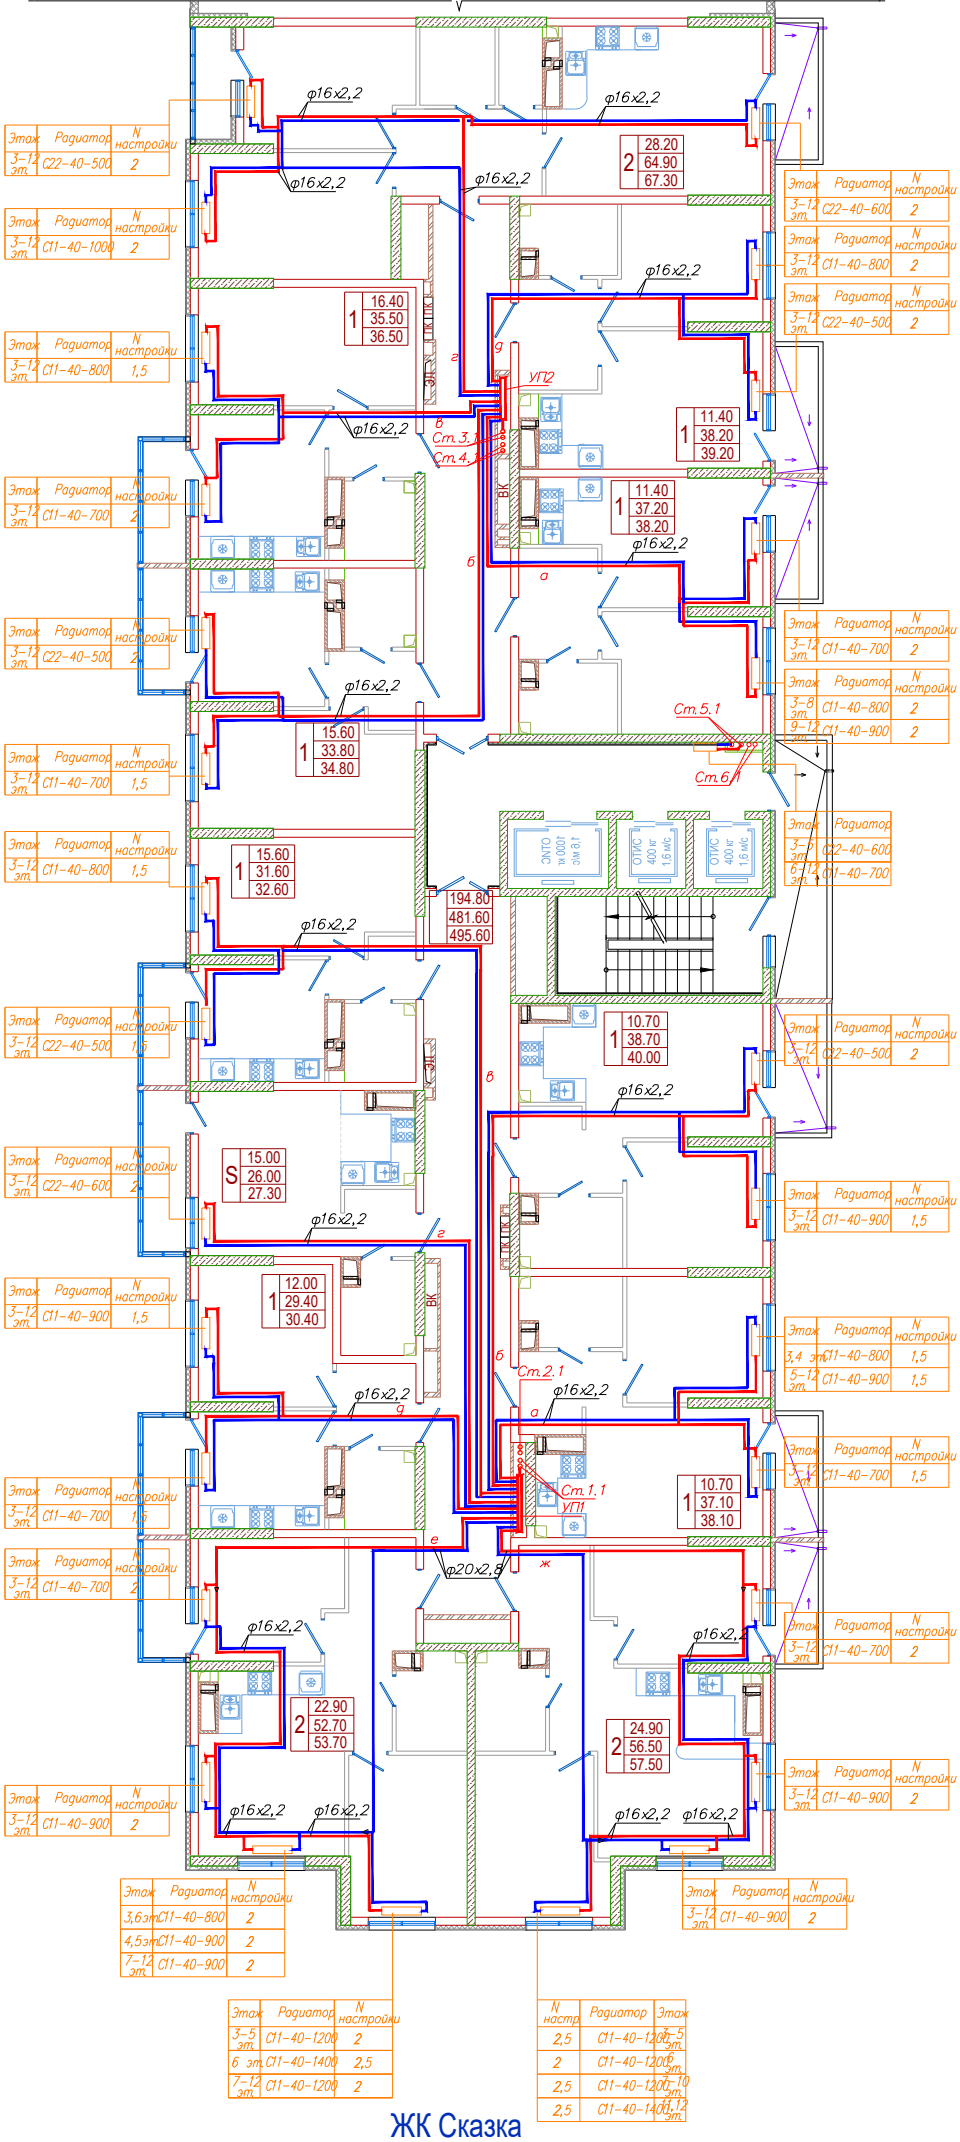

ЖК Сказка

БС1. Поквартирная этажная разводка отопления

План 3-12 этажа